
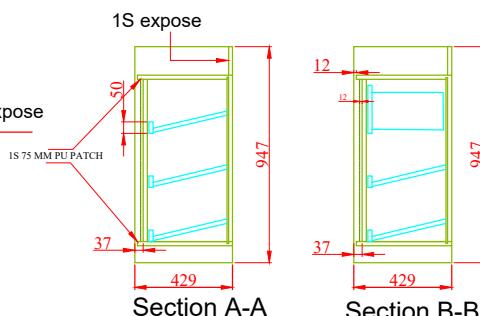
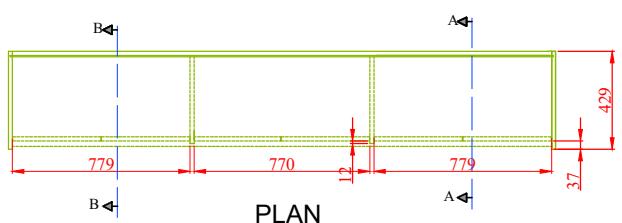
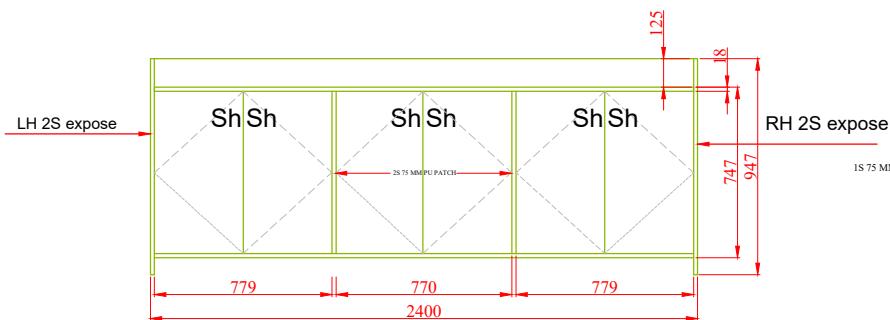


SHOE RACK

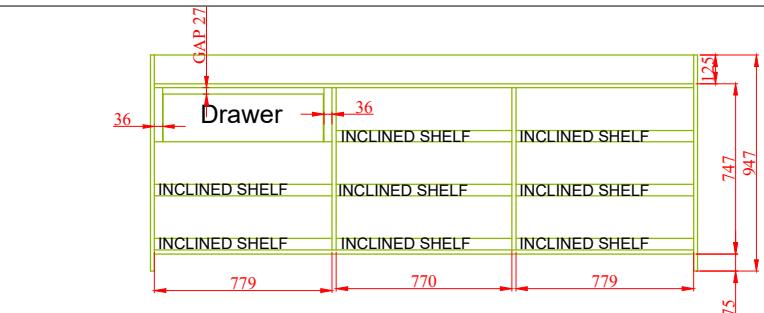

REFERENCE IMAGE

CARCASE :-
ALL BASE MATERIAL ARE IN 18/18 MM THK MDF 2S PRELAM WHITE


CONSTRUCTION AS PER RAWING:-INCLIND SHOE SHELF & INTERNAL DRAWER

EXPOSE :-
EXTREME LHS & RHS PANELS ARE IN 18MM THK MDF EXPOSE IN 2S PU CARAMEL TAN MATT BACK & INSERT ADD ON PANELS & BOTTOM PANEL IN 18MM THK MDF 75 MM PU PATCH WHITE MATT AS PER DRAWING
TOP PANEL 18 MM THK MDF 1S PU CARAMEL TAN MATT 1S 75 MM PU PATCH AS PER DRAWING


SHUTTER :-
ARE IN 18MM THK MDF EXPOSE IN 1S PU CARAMEL TAN MATT 1S PRELAM WHITE

HARDWARE :-
SOFT CLOSE HINGES FROM HETTICH CONSIDERED.
SOFT CLOSE TELESCOPIC CHANNELS FROM HETTICH CONSIDERED.


TV UNIT

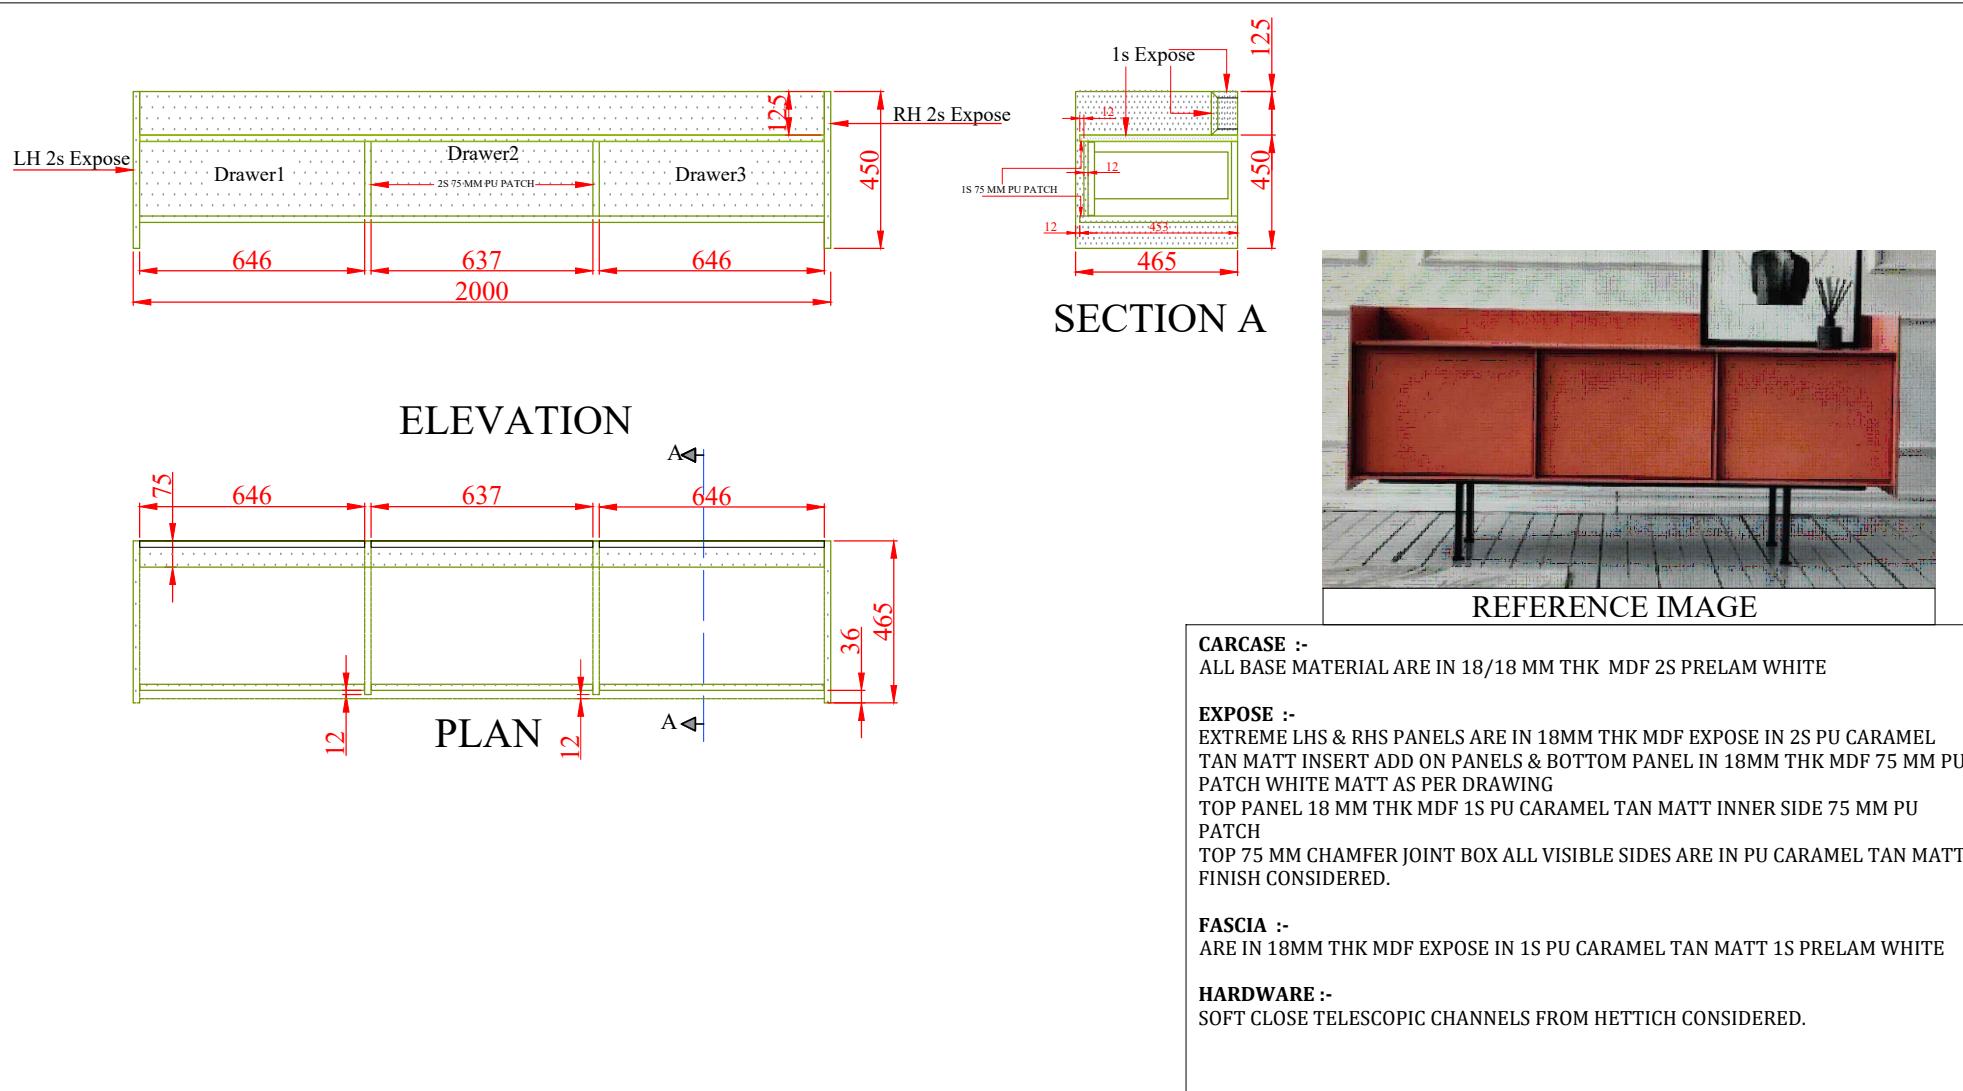


CROCKERY UNIT

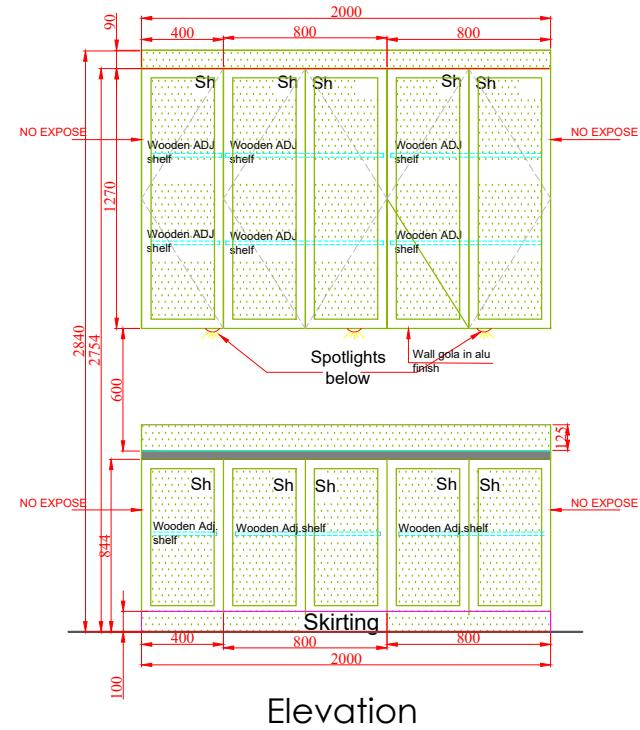

Elevation

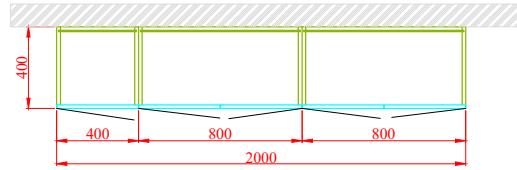

Plan

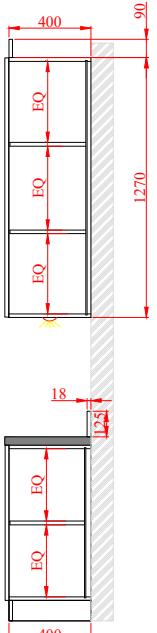

SECTION-B-B

CARCASE :-

ALL BASE MATERIAL ARE IN 18/18 MM THK HDF 2S PRELAM TEAK WALNUT - 3425

EXPOSE :-

SKIRTINGS & FILLERS ARE IN 18MM THK HDF EXPOSE IN 1S SLATE GREY PU MATT 1S PRELAM TEAK WALNUT - 3425

SHUTTER :-NON STD ROUTED

ARE IN 25 MM HDF 1S SLATE GREY PU MATT

HARDWARE :-


SOFT CLOSE HINGES FROM HETTICH CONSIDERED.


WARM WHITE SPOT LIGHTS FROM EBCO CONSIDERED.(S-BRRR-NW)

LIBRA H1 WALL HANGING BRACKETS FROM HAFELE CONSIDERED.

125 MM FRONT PANEL FIXING ON SITE


CROCKERY AND BAR UNIT

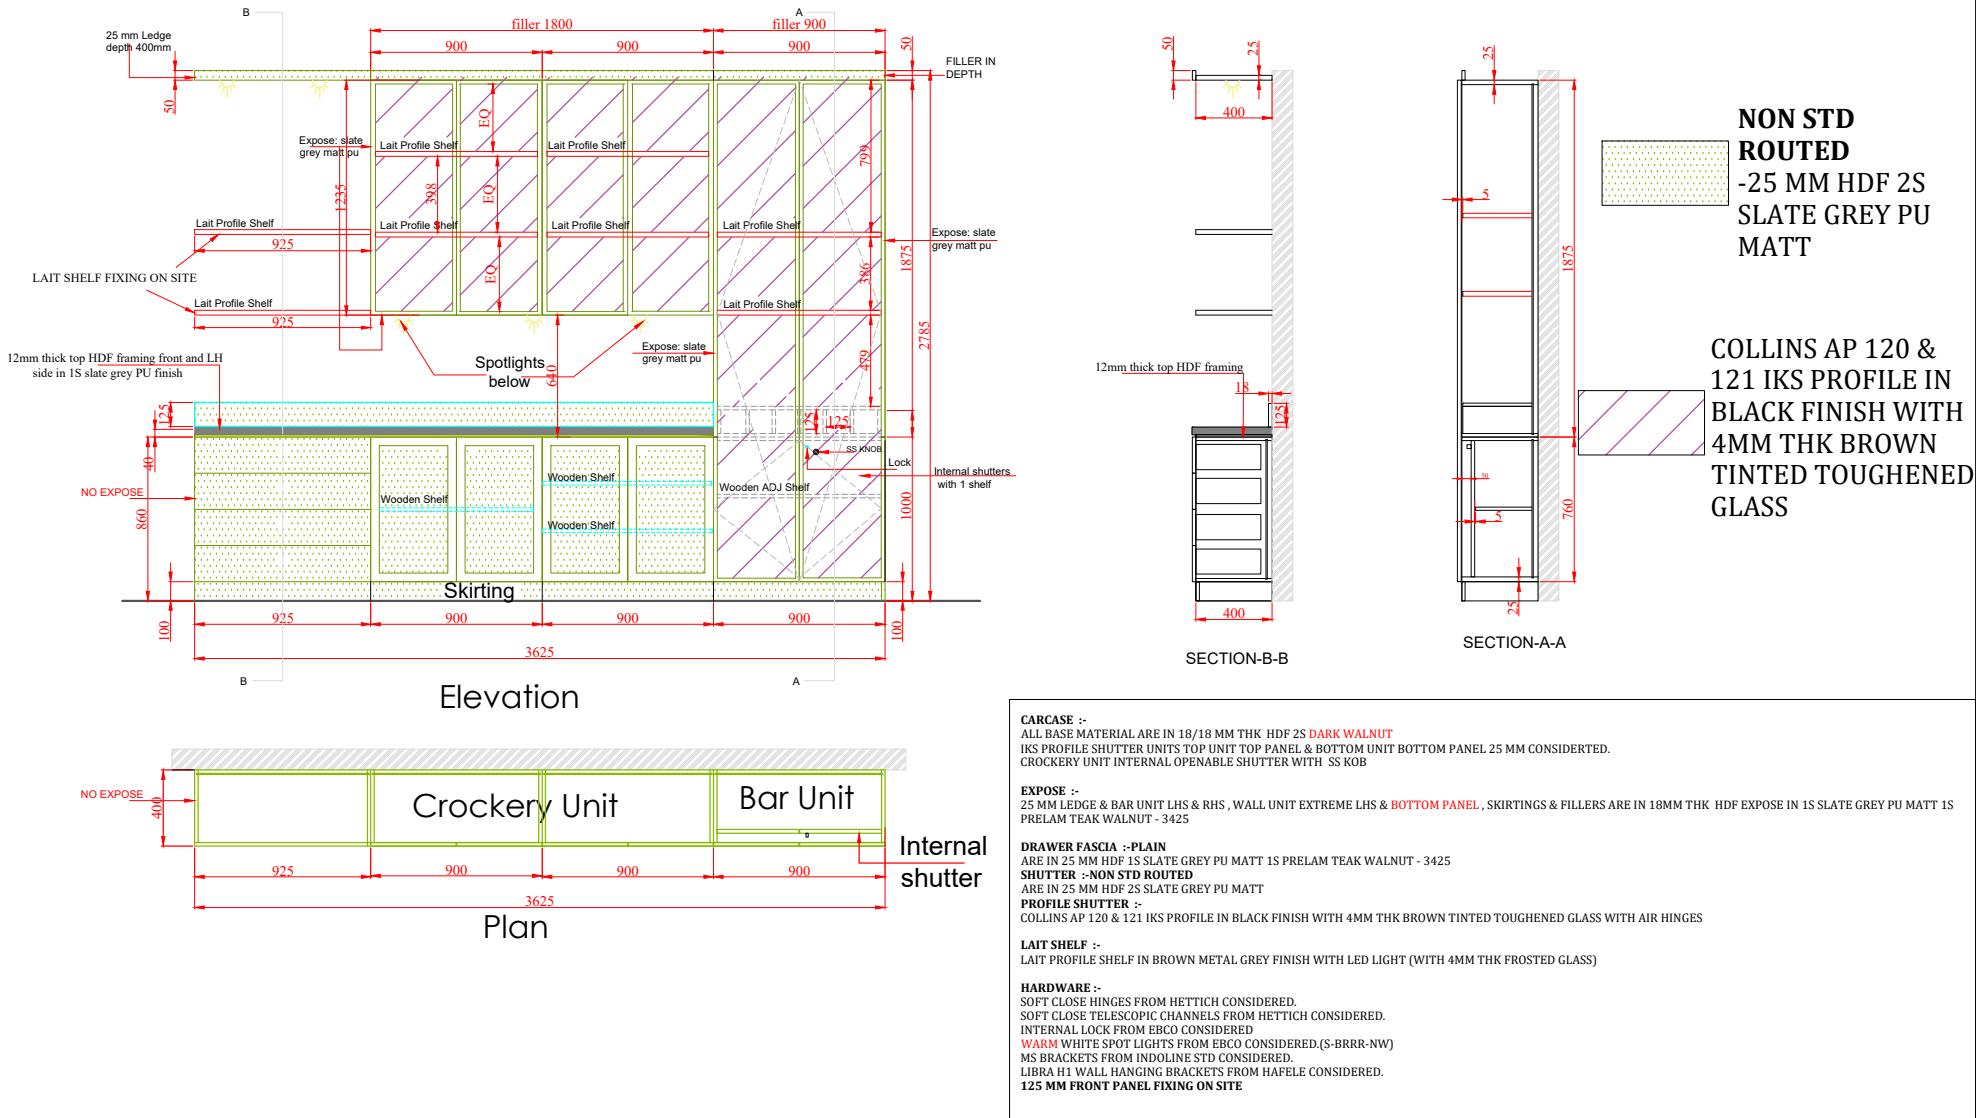

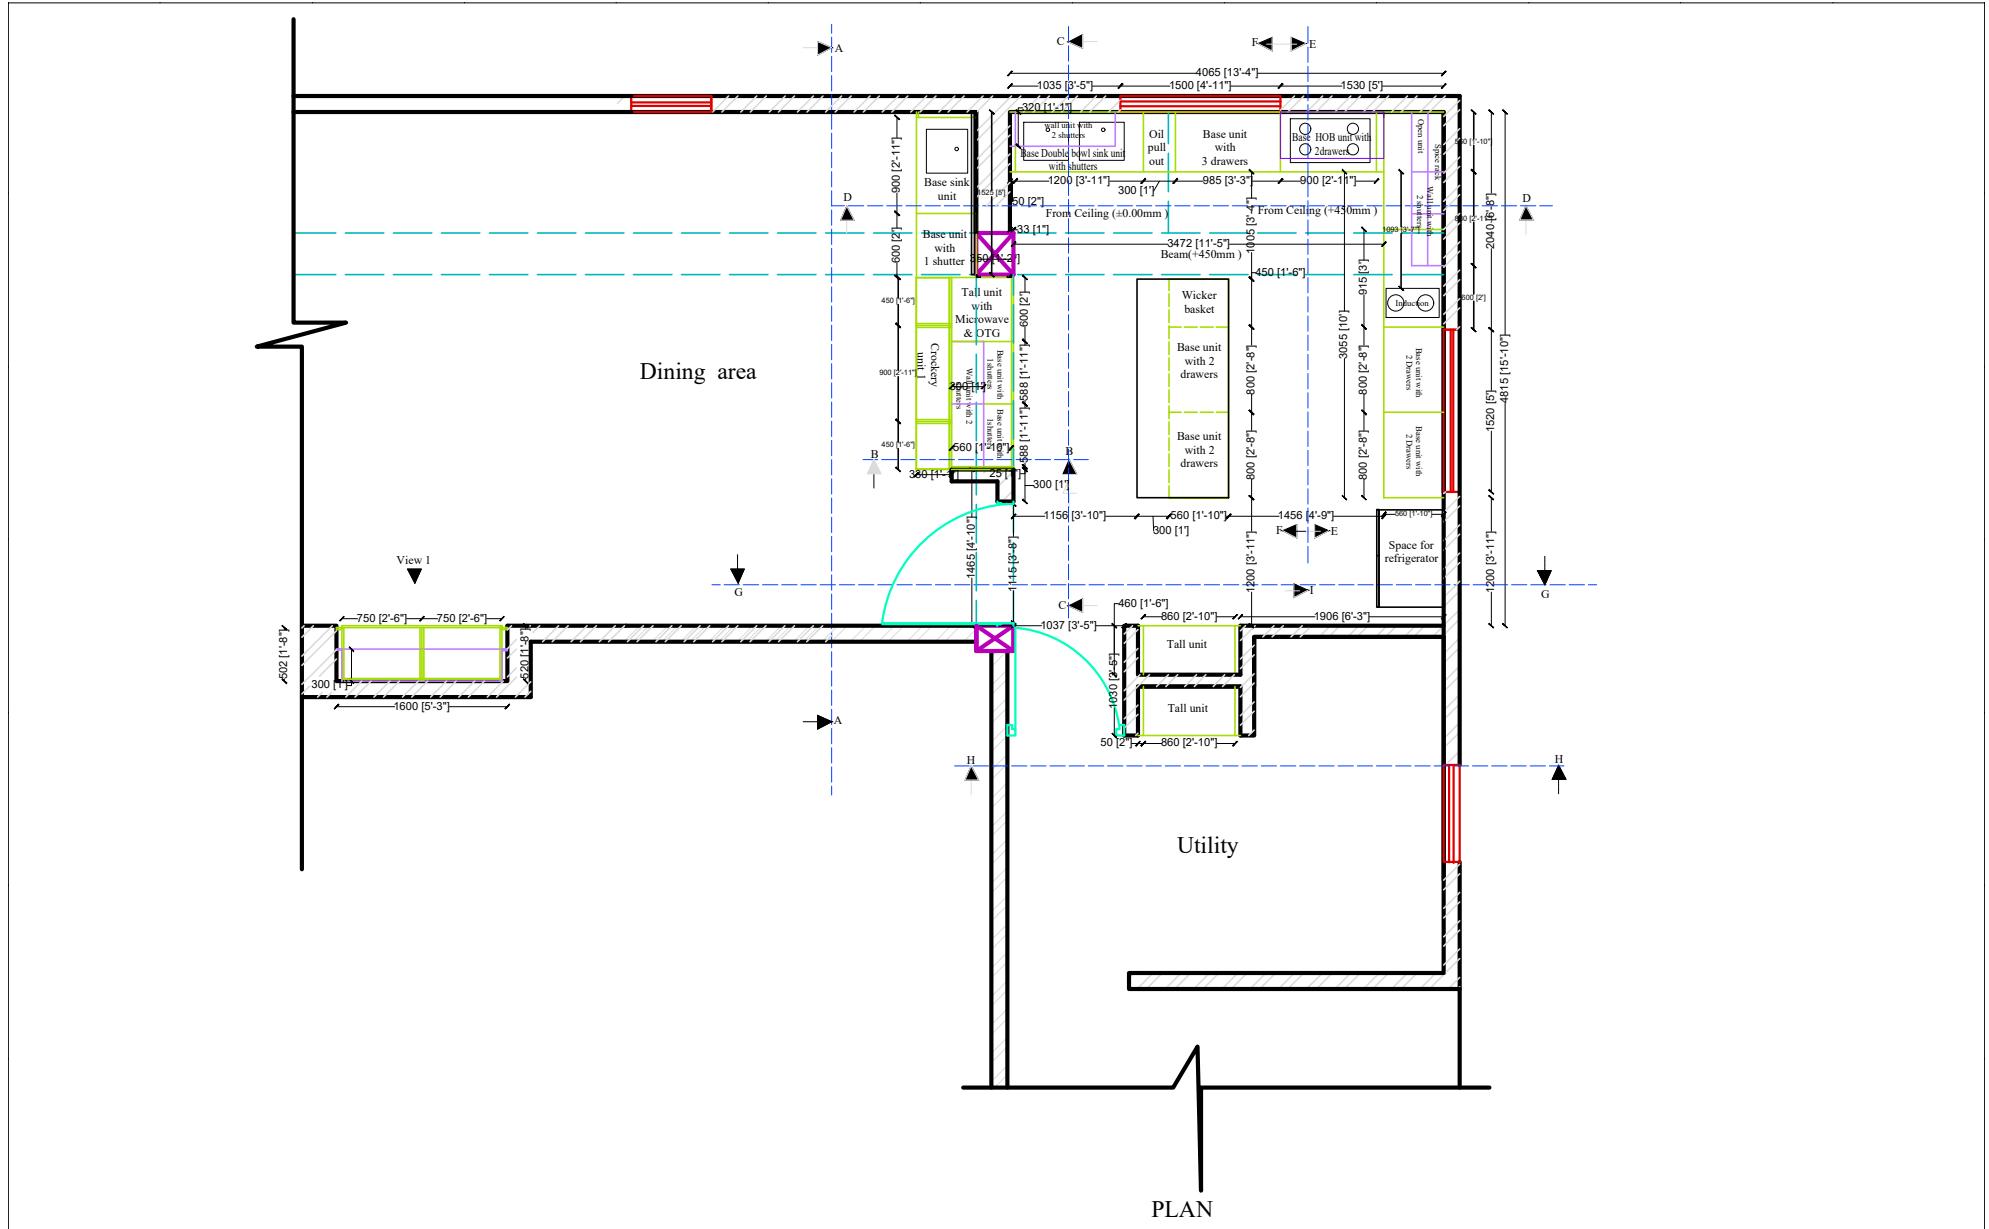









KITCHEN DETAILED PLAN -2D DRAWING

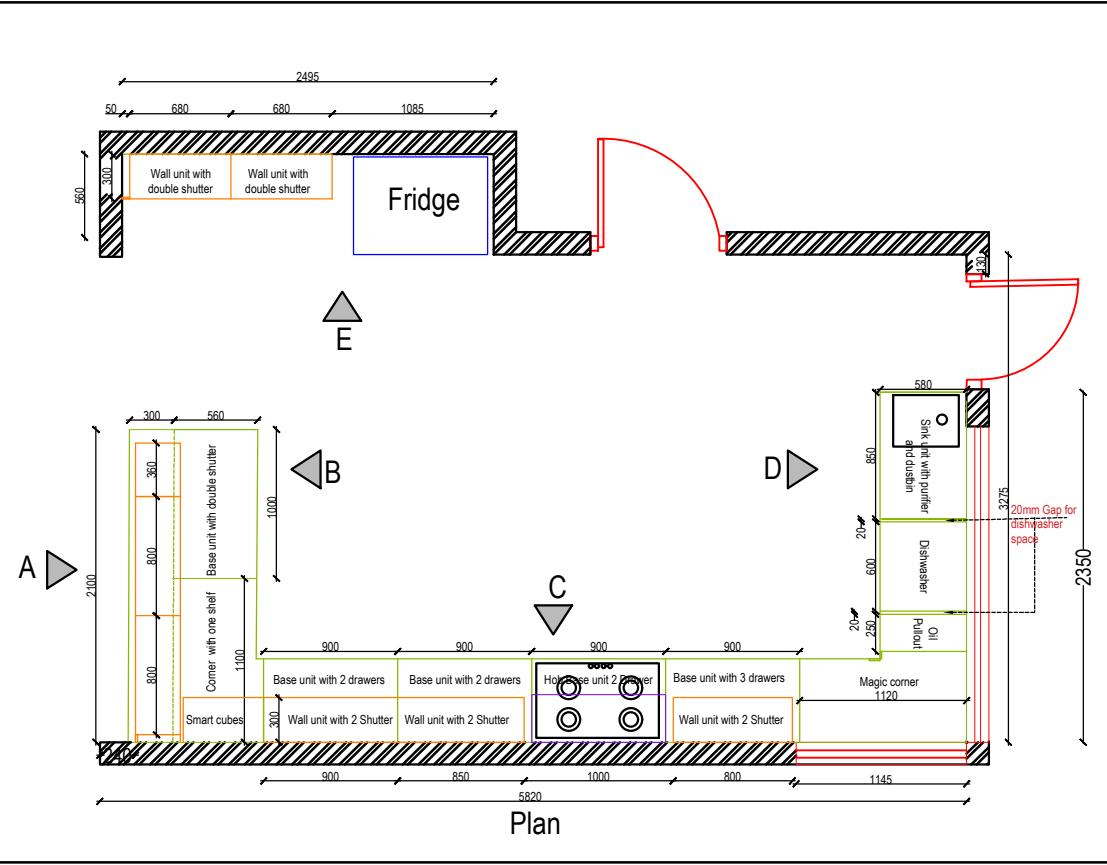


- Kitchen base unit carcass- BWP (water boiling proof), White finish internal.
Carcass edge – Matching dust strip.
- Handles- L & C gola in black pu matt finish.
- Kitchen base unit shutter – BWP , **Etheral Glossy pu finish .**
- Kitchen wall unit carcass: BWP , white finish internal.
Handle – Wall Gola in alum finish with two way slim led light with sensor .
- Kitchen wall unit shutter- BWP, **Lyric Blue pu Glossy finish .**
- Lift up shutter – **Sky Marble exclusive laminate finish .**
- Crockery unit carcass : BWP , Carmeo finish internal.
Crockery unit shutter : MU001 profile with handle, profile in **black pu matt and brown tinted glass.**
- LED: Slim warm Led light .
- Cube's: Black painted with Carmeo finish shelf with bottom warm LED light.

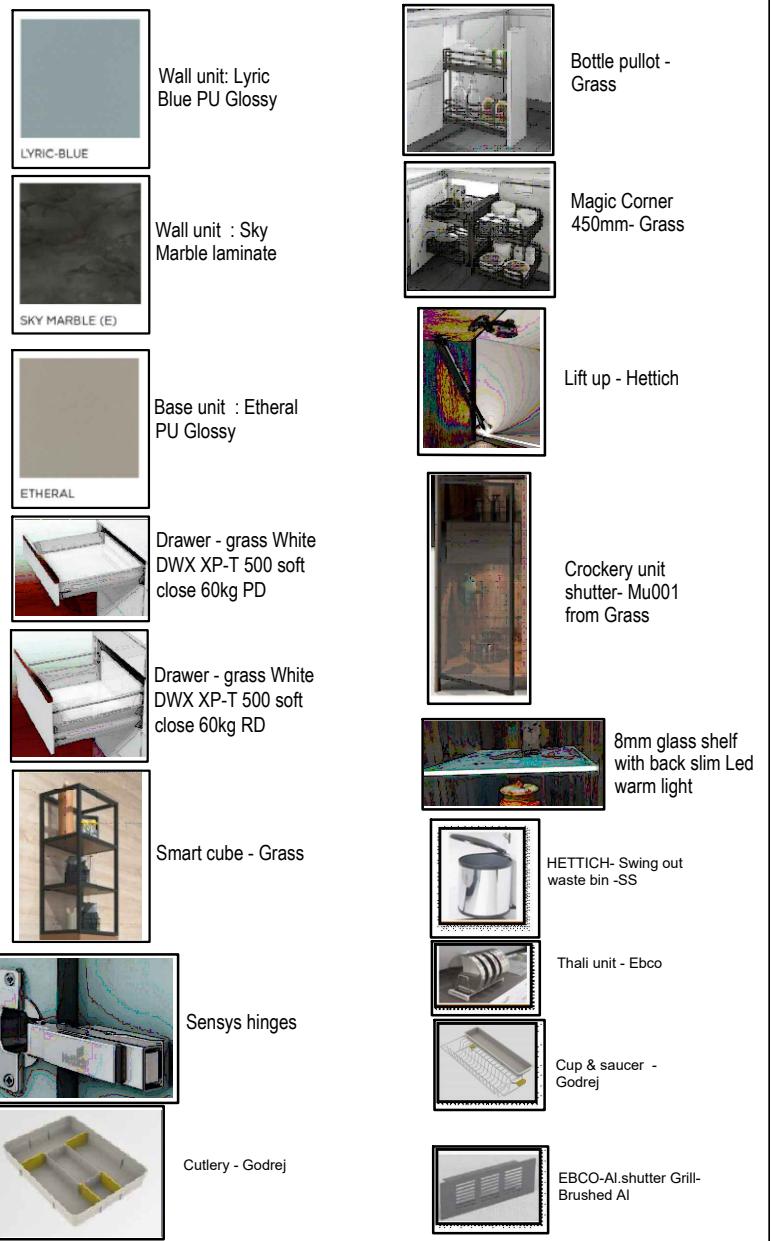


KITCHEN ELEVATION DRAWING

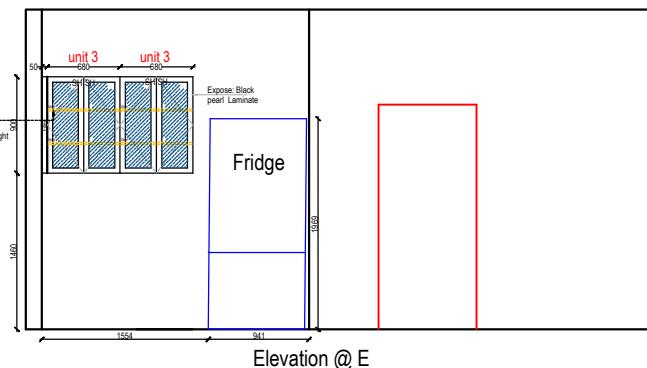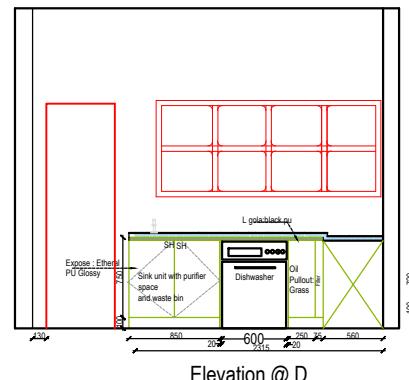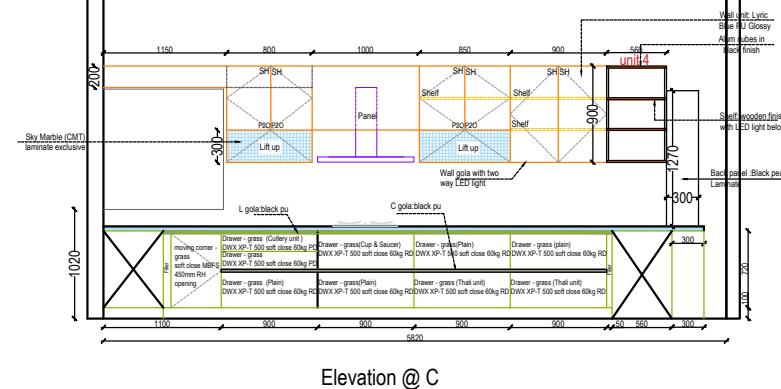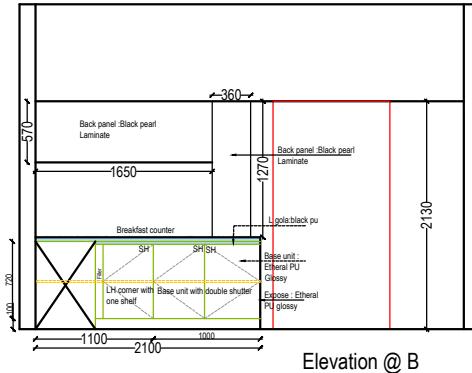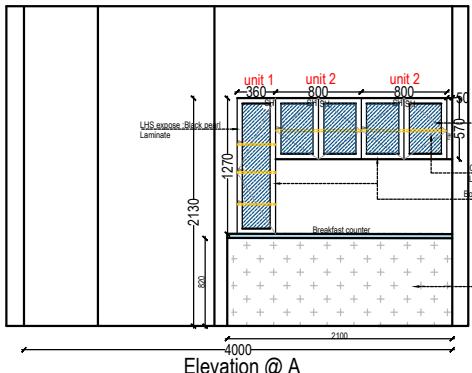


L & C GOLA CUTOUT DRAWING

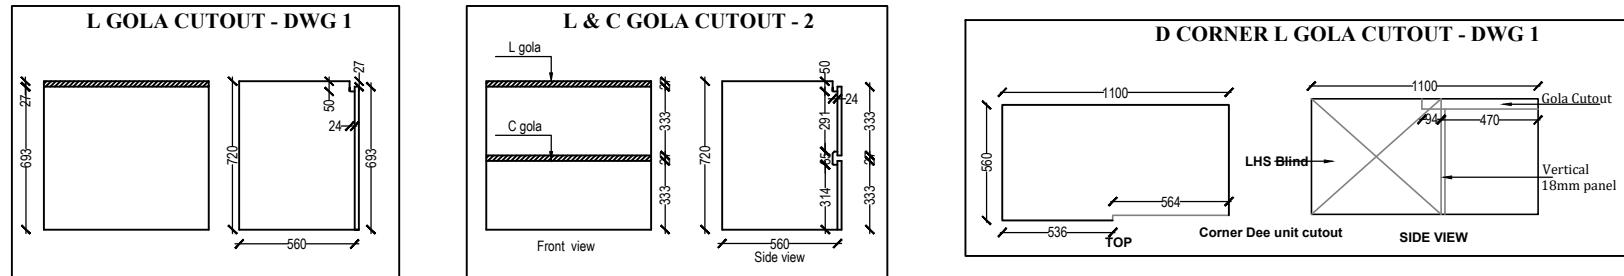



PANEL GROOVING DRAWING

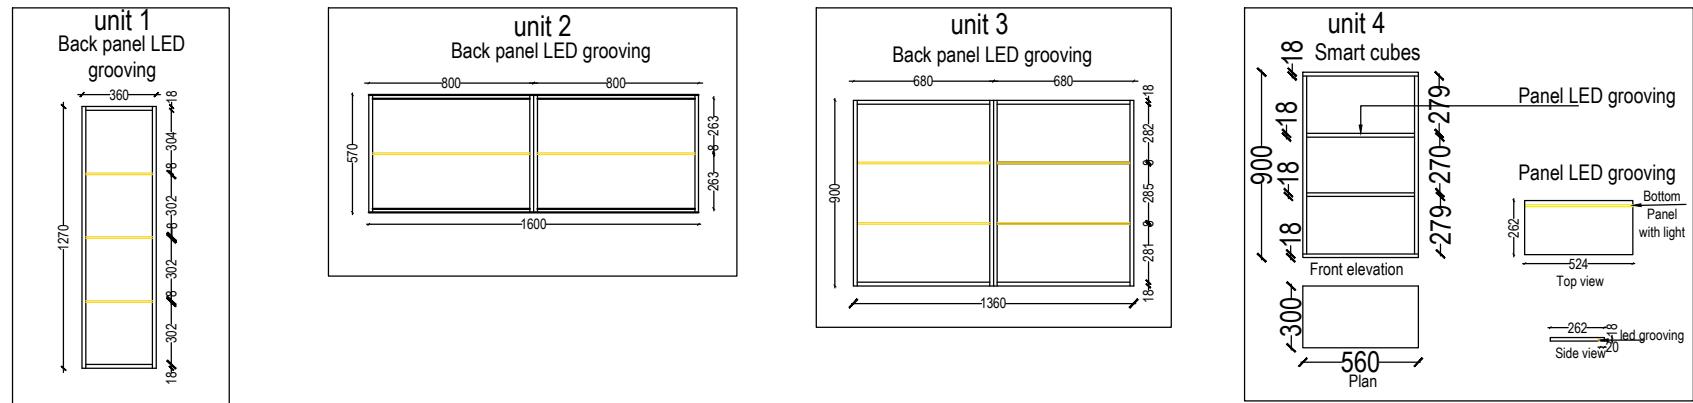


MU001 SHUTTER

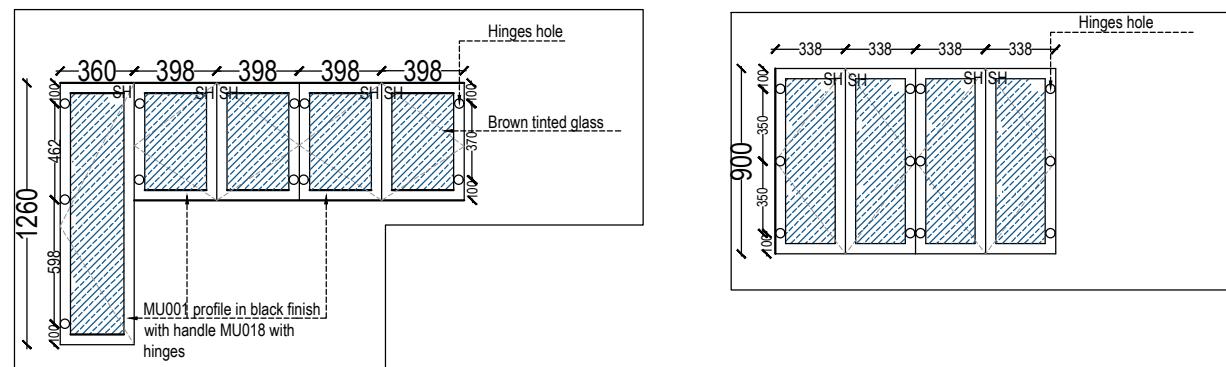

WARDROBES

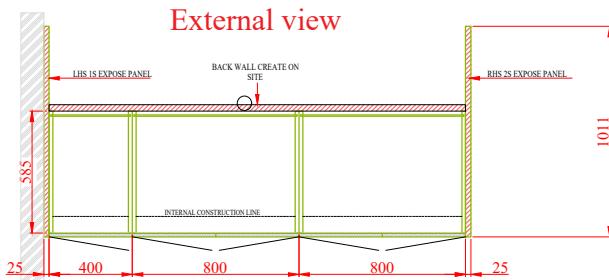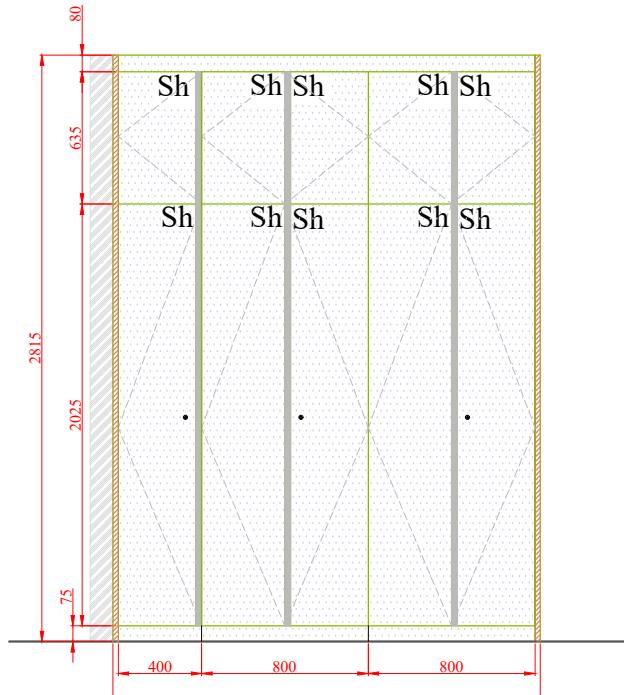

Plan

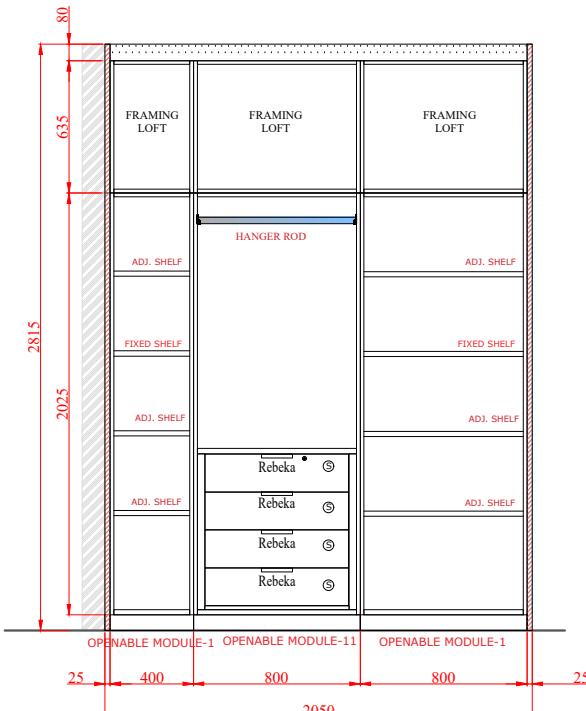

NOTE:-FRAMING LOFT CONSIDERED

CARCASE :-
ALL BASE MATERIAL ARE IN 18/18 MM THK MDF 2S PRELAM WHITE
DRAWER FASCIA :-REBEKA

EXPOSE :-
EXTREME LHS 1S & RHS 2S 25 MM THK MDF ADD ON PANELS 1011 DEPTH IN SLATE GREY PU MATT BACKING PRELAM WHITE
FILLERS & FRONT SKIRTINGS ARE IN 18MM THK MDF EXPOSE IN 1S DUST BLUE PU MATT 1S PRELAM WHITE

SHUTTER :- 8 X 4 PLUS LOFT
ARE IN 18 MM THK HDF EXPOSE IN 1S DUST BLUE PU MATT (WITH J SECTION IN TITANIUM GREY(METALLIC))

HARDWARE :-
SOFT CLOSE HINGES FROM HETTICH CONSIDERED.
SOFT CLOSE TELESCOPIC CHANNELS FROM HETTICH CONSIDERED.
STD DOOR STRAIGHTENER CONSIDERED.
SS HANGER ROD FROM HETTICH CONSIDERED.
2 POINT DOOR LOCK FROM UTTURKAR CONSIDERED.
DRAWER LOCK FROM EBCO CONSIDERED (ONLY FOR TOP DRAWER)

